

## Plano de Instalaciones Electricasluminacion

\* \* \*
Fondo Hondureño
de Inversión Social
FHIS
Gottemo de la República

PROYECTO: Restauracion Alcaldia Municipal de El Naranjito

UBICACIÓN: Casco urbano, Alcaldia, El Naranjito,

PLANO ELECTRICO ESCALA: HO
1:100

FECHA: Febrero/ 2023


HOJA: CODIGO: 109639

24 INST/: FHIS



EV/FM:

DIRECCIÓN DE PROVECTOS

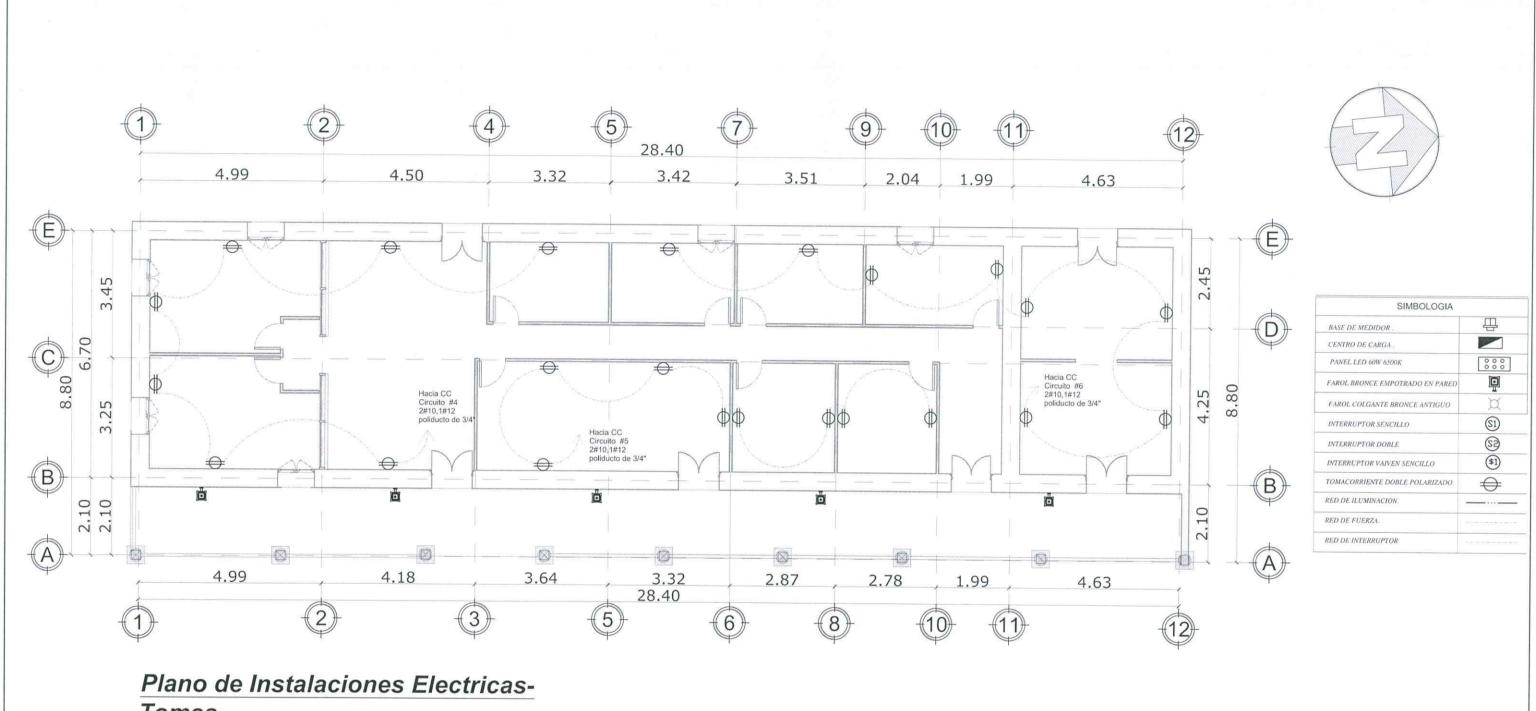

**Tomas** 

Fondo Hondureño de Inversión Social FHIS

PROYECTO: Restauracion Alcaldia Municipal de El Naranjito

UBICACIÓN: Casco urbano, Alcaldia, El Naranjito, Santa Barbara.

**PLANO ELECTRICO** 

ESCALA: 1:100 FECHA: Febrero/ 2023

HOJA: 22 24

CODIGO: 109639 INST/: **FHIS** 



DIRECCIÓN DE BROYET